


C:\Users\koster\Documents\Online_FSB-NEW_Central_R18_allenfordster.txt	
--	--

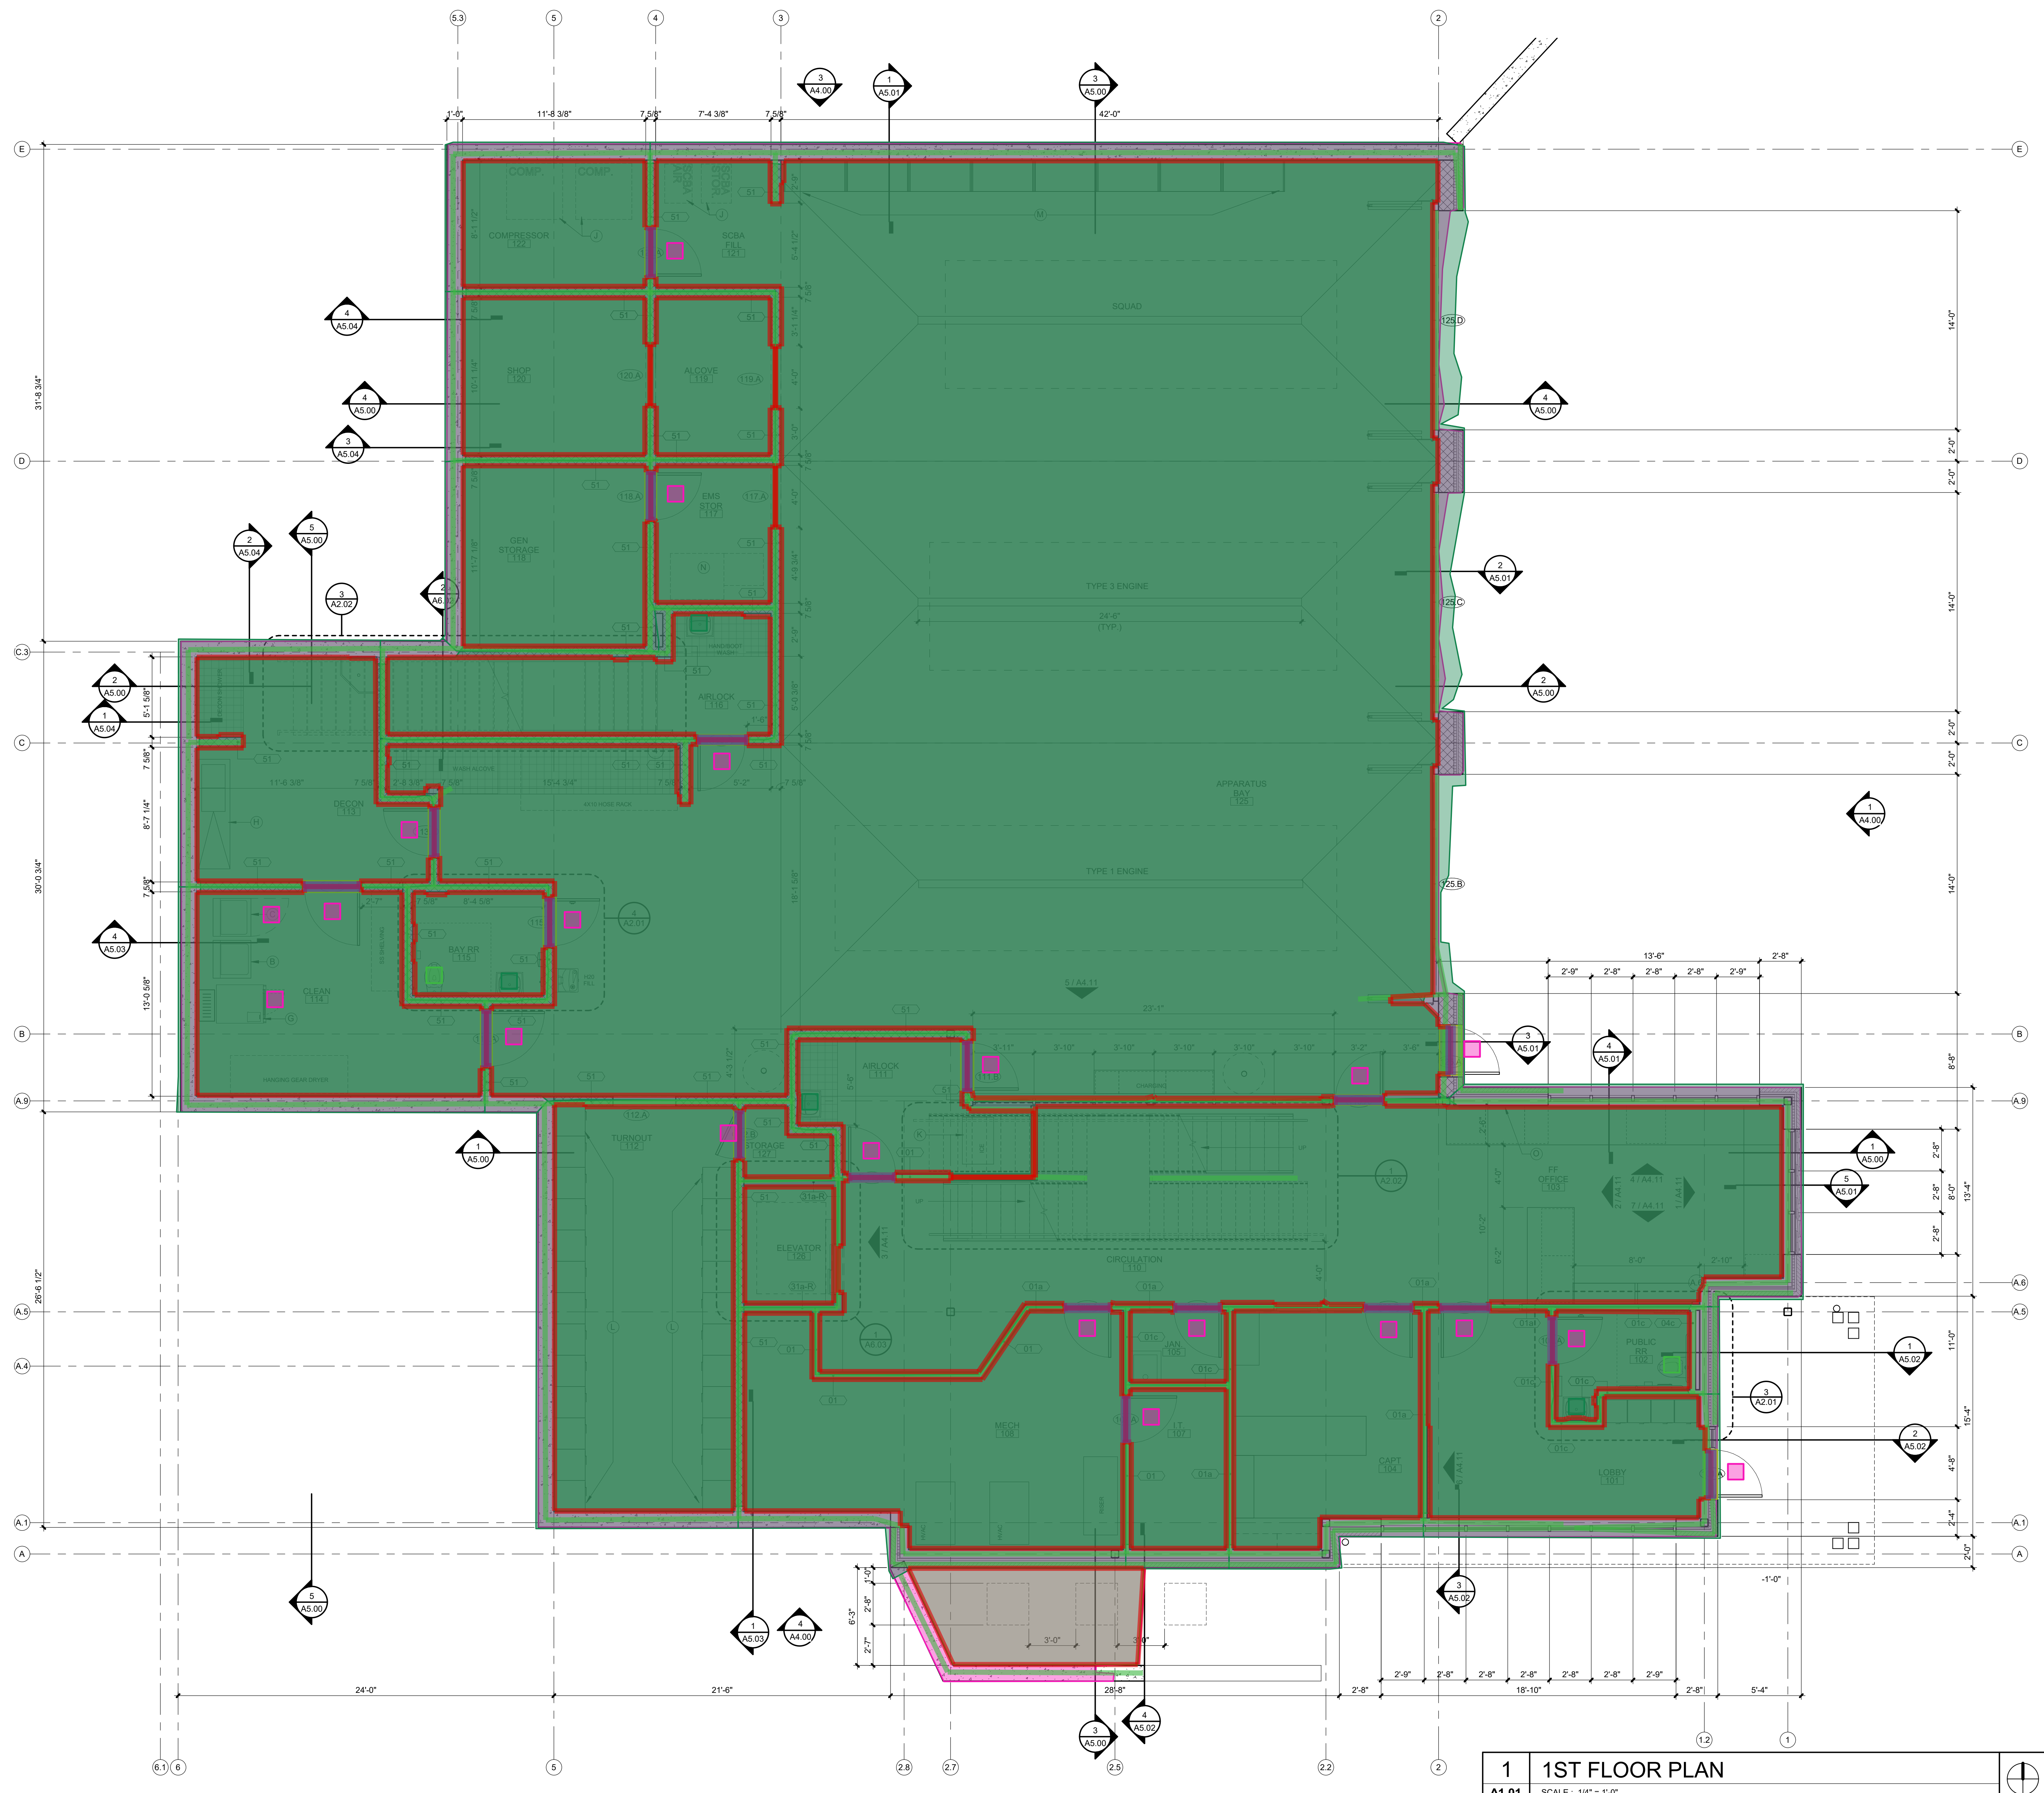

Olathe Fire
Station No. 8
14700 Lakeshore Dr
Olathe KS



No.:	19003
	02.17.2020
For:	DESIGN DEVELOPMENT

[illegible]

REGISTRATION

FOR CONSTRUCTION

PROJECT TEAM

ECT FINKLE+WILLIAMS
ARCHITECTURE

TCA ARCHITECTS

SK DESIGN GR

CAPE SWT DESIGN

TURAL BOB D. CAMPE

LANKFORD | FI

NICK LANKFORD | FIDELITY INVESTMENTS

LANKFORD | F

ACTOR TURNER CONS

KLE + WILLIAM
ARCHITECTS

College Blvd, Suite
and Park, Kansas 66
98-1550


SHEET TITLE

FIRST FLOOR PLAN

SHEET NUMBER

A1.01

Total areas		
	Footprint 1	7,208 SF
	Net area 30	6,547 SF
	Doors area 25	51 SF
	Gross area 29	7,262 SF
	Gross Internal Area ...	296,803 SF
Total lines		
	Doors centerline 25	76 FT
	Wall centerline 154	1,032 FT
	Wall Perimeter 30	1,466 FT
Total counts		
	Toilet 5	5 EA
	Sink 5	5 EA
	Single Swing Door 25	25 EA
	Double Swing Door 11	11 EA
	Urinals 1	1 EA
	Cooktop 1	1 EA

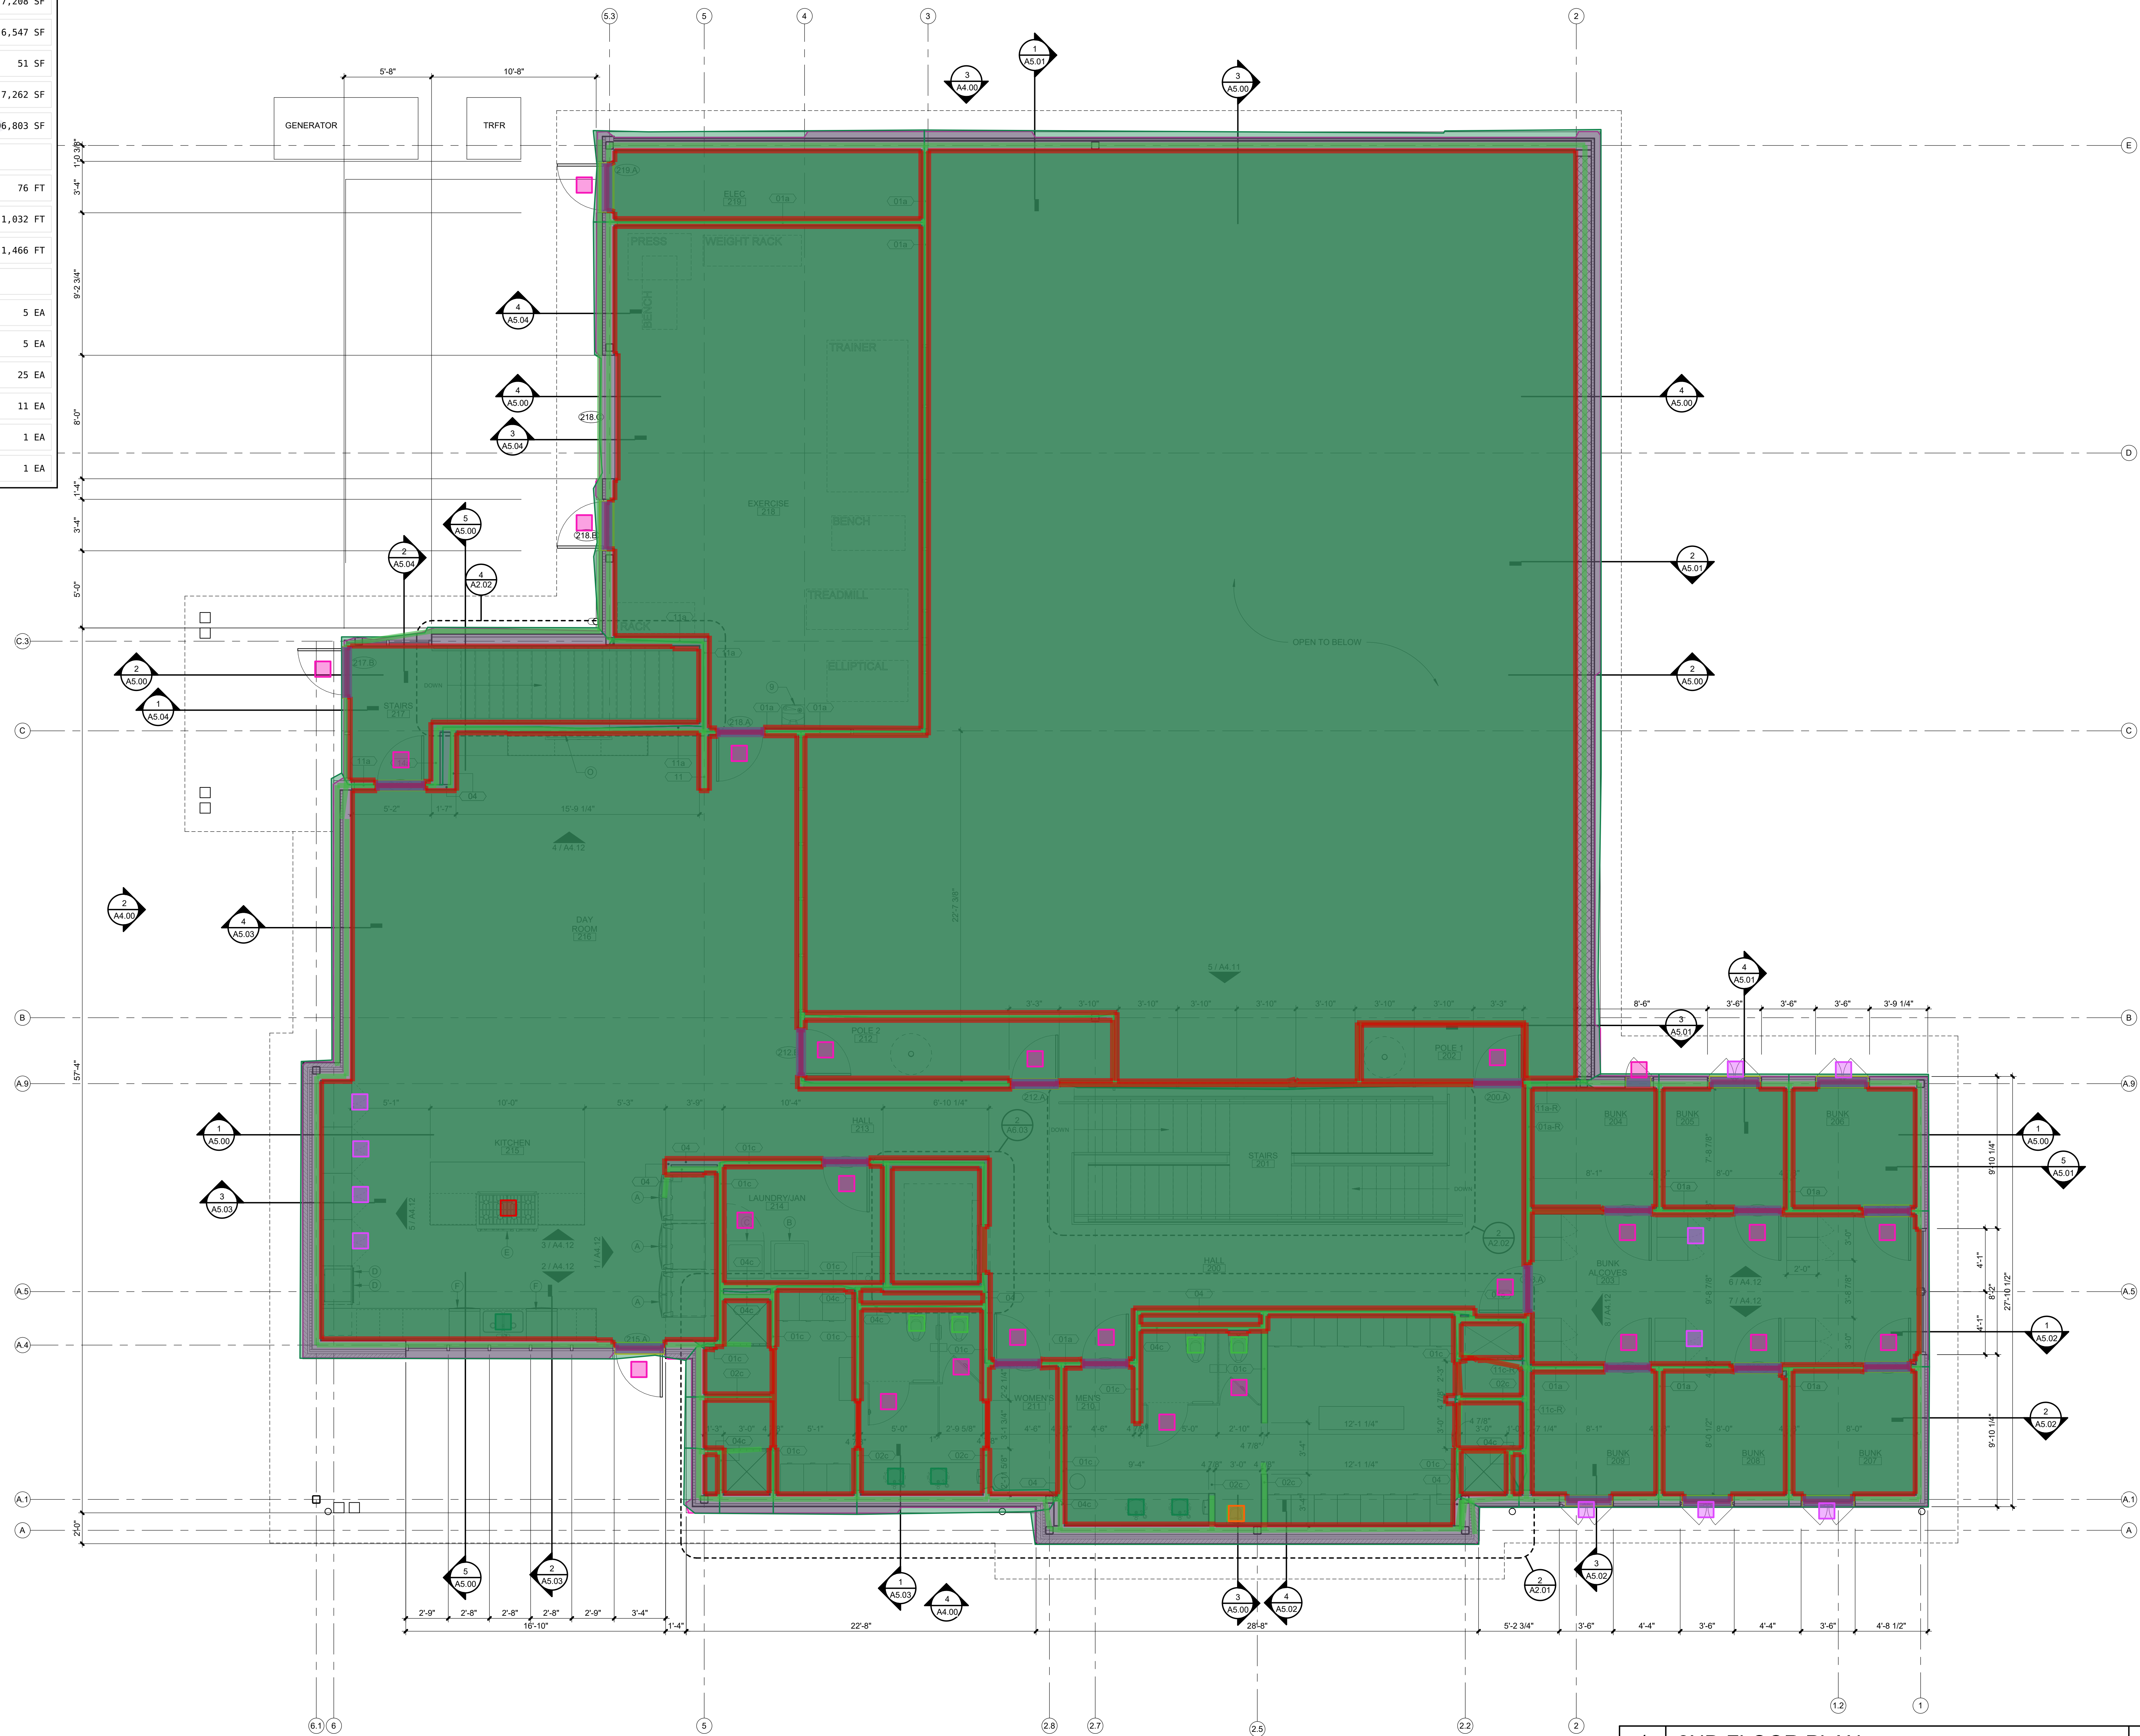

Olathe Fire
Station No. 8
14700 Lakeshore Dr
Olathe KS



Project No.:	19003
Date:	02.17.2020
Issued For:	DESIGN DEVELOPMENT

[illegible]

REGISTRATION

NOT FOR CONSTRUCTION

PROJECT TEAM	
ARCHITECT	FINKLE+WILLIAMS ARCHITECTURE
FIRE STATION CONSULTANT	TCA ARCHITECTURE
CIVIL	SK DESIGN GROUP
LANDSCAPE	SWT DESIGN
STRUCTURAL	BOB D. CAMPBELL
PLUMBING	LANKFORD FENDLER
MECHANICAL	LANKFORD FENDLER
ELECTRICAL	LANKFORD FENDLER
CONTRACTOR	TURNER CONSTRUCTION

FINKLE + WILLIAMS
ARCHITECTURE

7007 College Blvd, Suite 411
Overland Park, Kansas 66211
913+498-1550

SHEET TITLE

SECOND FLOOR PLAN

SHEET NUMBER

A1.02

